MA'ADEN معادن

Saudi Arabian Mining Company شركة التعدين العربية السعودية

Project **Mansourah Massarah Gold Project**
Customer: **MA'ADEN GOLD AND BASE METALS (MA'ADEN)**

Title: **CALCULATION**
3850 REAGENTS – LIME SLAKING EQUIPMENT
MILK OF LIME DOSING TANK

Document Number: **MD-216-3850-EG-CV-CAL-1430**

Revision: **D01**

Revision Date: **14.11.2023**

Status: **AS BUILT**

Outotec Document Number:	900707	GAU01	AA03	CED01	38503	OU100688398	2
L&T Document Number:	O19045	450	C	K	24166	001	2

REVISION HISTORY

Rev	Date	Revision Text	Prepared By	Reviewed By	Approved By	Employer
A01	25.06.2020	FIRST ISSUE	SUE	BDA	AG	
C01	21.07.2020	ISSUED FOR CONSTRUCTION	SUE	BDA	AG	
DO1	14.11.2023	AS BUILT	SUE	BDA	AG	

MA'ADEN معادن Saudi Arabian Mining Company شركة التعدين العربية السعودية		Outotec / LARSEN & TOUBRO
MD-216-3850-EG-CV-CAL-1430	Mansourah Massarah Gold Project	Page OF
900707_GAU01_AA03_CED01_ 38503_OU100688398_R2	CALCULATION REAGENTS – LIME SLAKING EQUIPMENT MILK OF LIME DOSING TANK	Date 14.11.2023
O19045_450_C_K_24166_001_R2	AS BUILT	Rev. D01

TABLE OF CONTENTS **PAGE NO**

DEFINITIONS AND ABBREVIATIONS 3

1 INTENT 4

2 EXECUTIVE SUMMARY 4

3 SCOPE 4

4 DESIGN REQUIREMENTS
- 4.1 Reference Codes & Books 4
- 4.2 Materials Property 4
- 4.3 Minimum Reinforcing Steel (Rebar) Size 5
- 4.4 Concrete Clear Cover 5

5 LOADS
- 5.1 Primary Loads 5
- 5.2 Load Combinations for Stress Calculation 5
- 5.3 Load Combinations for Strength Calculation 5

6 SAFETY FACTOR AGAINST STABILITY
- 6.1 Against Overturning 6
- 6.2 Against Sliding 6

7 ALLOWABLE SOIL BEARING CAPACITY 6

8 DESIGN OF TANK FOUNDATION (3850-REA-001 MILK OF LIME DOSING TANK) 7

ATTACHMENT - 1 : MECHANICAL INPUT DRAWING. 11

PROPRIETARY & CONFIDENTIAL

The contents of this document are the sole property of Outotec Oyj. Any rights not expressly granted herein are reserved. Reproduction, transfer or distribution of part or all of the contents in any form without the prior written permission of Outotec is prohibited.

This document is the property of LARSEN & TOUBRO and must not be passed on to any person or body not authorized by us to receive it nor be copied or otherwise made use either in full or in part by such person or body without our prior permission in writing.

MA'ADEN معادن Saudi Arabian Mining Company شركة التعدين العربية السعودية		Outotec / LARSEN & TOUBRO
MD-216-3850-EG-CV-CAL-1430	Mansourah Massarah Gold Project	Page OF
900707_GAU01_AA03_CED01_ 38503_OU100688398_R2	CALCULATION REAGENTS – LIME SLAKING EQUIPMENT MILK OF LIME DOSING TANK	Date 15.11.2023
O19045_450_C_K_24166_001_R2	AS BUILT	Rev. D01

DEFINITIONS AND ABBREVIATIONS

Document	:	Information and the medium on which it is contained (ISO 9000:2015)
EMPLOYER	:	EMPLOYER' means MA'ADEN GOLD AND BASE METALS (MGBM) and the PMC American Bechtel Inc. or their representatives
Contractor	:	Contractor' means consortium composed of LARSEN & TOUBRO LIMITED, Saudi Arabia AND OUTOTEC SAUDI ARABIA LLC, Saudi Arabia (for IK Contract) and LARSEN & TOUBRO LIMITED – ECC Construction Group – (SHJ BR) and OUTOTEC ENGINEERING DMCC, Dubai (for OOK Contract).
'PMT'	:	Ma'aden Project Management Team
'MMGP Project'	:	Mansourah Massarah Gold Processing Project
Attribute	:	Information element that describes a document or tag.
Supplier	:	An entity (supplier, consultant, sub-contractor) under the direct project management of Contractor
Sub-Supplier	:	A sub entity (supplier, consultant, sub-contractor) under the direct project management of Contractor.
QA	:	Quality Assurance
QC	:	Quality Control
Works	:	Full scope of the EPC Contract including the engineering, procurement, construction, commissioning and associated activities

PROPRIETARY & CONFIDENTIAL

The contents of this document are the sole property of Outotec Oyj. Any rights not expressly granted herein are reserved. Reproduction, transfer or distribution of part or all of the contents in any form without the prior written permission of Outotec is prohibited.

This document is the property of LARSEN & TOUBRO and must not be passed on to any person or body not authorized by us to receive it nor be copied or otherwise made use either in full or in part by such person or body without our prior permission in writing.

MD-216-3850-EG-CV-CAL-1430	Mansourah Massarah Gold Project	Page OF
900707_GAU01_AA03_CED01_ 38503_OU100688398_R2	CALCULATION REAGENTS – LIME SLAKING EQUIPMENT MILK OF LIME DOSING TANK	Date 15.11.2023
O19045_450_C_K_24166_001_R2	AS BUILT	Rev. D01

1. INTENT

The Purpose of this document is to analysis & design of **3850-REA-001 MILK OF LIME DOSING TANK**
The dimensions and reinforcement are to be calculated. The report describes the methodology and the design parameters used in the design calculation. The analysis & design is carried out in accordance with project specifications , codes & standards.

2. EXECUTIVE SUMMARY

The Saudi Arabian Mining Company (Ma'aden) has announced that its wholly-owned subsidiary, Ma'aden Gold and Base Metals Company, have issued a Notice of Award to Outotec and Larsen & Toubro Consortium to complete the engineering, procurement, construction, pre-commissioning, commissioning and start-up assistance of the Mansourah & Massarah (MMGP) Gold Project.

MMGP project will become Ma'aden's largest ever gold project, producing an average of 250,000 ounces of gold per year over the life of mine. Mansourah- Massarah is situated within the Central Arabian Gold Region (CAGR), approximately 320km northeast of Taif towards Riyadh and about 35 km southeast of Hufairah, which is a small village situated on Jeddah - Riyadh highway. Mansourah - Massarah gold deposits are located 22°38'6.40"N; 42°44'22.90"E, and 22°42'1.40"N; 42°41'58.40"E respectively, approximately 537 km east of Jeddah and 77 km southeast of the town of Zalim.

The plant throughput capacity is 4000000t/a and is required to operate on a continuous basis at nominally 24 hours per day and 7 days a week.

3. SCOPE

The analysis has been carried out in standard excel sheet. Stability check against Overturning & Sliding are done in the excel sheet. Base Pressure check has been done in the excel sheet. For strength calculation Bending moment & Shear Force values are calculate in the conventional method & designed in the standard excel sheet.

4. DESIGN REQUIREMENTS

4.1 Reference Codes & Books

Reference is made in this standard as indicated in STRUCTURAL ENGINEERING DESIGN CRITERIA Doc No. : MD-216-1000-EG-ST-CRT-1001-A03 , Structural Design Criteria - Process Building & Structures ITB Doc No. : MD-101-SMEM-EG-ST-CRT-1001 & Civil Design Criteria - General ITB Doc. No. MD-101-SMEM-EG-CV-CRT-1001.

The below mention codes & books are also used for this design calculation.

(i) SBC - 301
(ii) SBC - 304 CR - 2018
(iii) ACI 318M.
(iv) ACI SP-17M(09)

4.2 Materials Property

A. Density

4.2.A.(i) Density of Dry Soil : 1.9 T/m^3
4.2.A.(ii) Density of Concrete : 2.5 T/m^3
4.2.A.(iii) Density of Water : 1.0 T/m^3

B. Concrete Grade

4.2.B.(i) Foundation and Structural Members: 35 Mpa Strength of 28 days
4.2.B.(ii) Blinding Concrete below foundation bases: 15 Mpa Strength of 28 days

C. Reinforcement Grade

4.2.C.(i) Deformed Bar : ASTM A 615 / A 615M Grade 60 (fy = 420MPa)
4.2.C.(ii) Welded Wire Fabric : ASTM A 185(Plain) / A 497(Deformed)

PROPRIETARY & CONFIDENTIAL
The contents of this document are the sole property of Outotec Oyj. Any rights not expressly granted herein are reserved. Reproduction, transfer or distribution of part or all of the contents in any form without the prior written permission of Outotec is prohibited.
This document is the property of LARSEN & TOUBRO and must not be passed on to any person or body not authorized by us to receive it nor be copied or otherwise made use either in full or in part by such person or body without our prior permission in writing.

D. Grout Grade

4.2.D.(i) Grout shall be 50 mm cementitious of Strength 40 MPa.

4.3 Minimum Reinforcing Steel (Rebar) Size

The minimum rebar size for use as tension, compression reinforcement shall be 12 mm, except where welded wire fabric is used. For ties and spirals the minimum rebar size shall be 10 mm.

4.4 Concrete Clear Cover

Concrete Exposure	Member	MinimumCove (mm)
Exposed to Soil	Foundation	50
	Wall	50
	Slab on Grade	20

5. LOAD

5.1 Primary Loads

3850-REA-001 MILK OF LIME DOSING TANK foundation design the primary load values are taken from **Drg. No. : MD-216-3850-EG-ME-PLN-1001**

1 DEAD LOAD OF EQUIPMENT (D)
2 EXTERNAL PLATFORM LOAD ($D_{platform}$)
3 OPERATIONAL WT. OF SLURRY ($F_{operating}$)
4 MAXIMUM WT. OF SLURRY (F_{max})
5 WIND LOAD (W)
7 SEISMIC LOAD (S)

5.2 Load Combinations for Stress Calculation

LOAD CASE	LOAD COMBINATION
101	$D + D_{platform} + F_{operation}$
102	$D + D_{platform} + F_{max}$
103	$D + D_{platform} + F_{operation} + W$
104	$D + D_{platform} + F_{max} + W$
105	$D + D_{platform} + F_{operation} + 0.7*E$
106	$D + D_{platform} + F_{max} + 0.7*E$
107	$0.6*(D + D_{platform}) + W$
108	$0.6*(D + D_{platform}) + 0.7*E$

5.3 Load Combinations for Strength Calculation

LOAD CASE	LOAD COMBINATION
201	$1.4*(D + D_{platform} + F_{operation})$
202	$1.4*(D + D_{platform} + F_{max})$
203	$1.2*(D + D_{platform}) + 0.8*W$
204	$1.2*(D + D_{platform}) + 1.6*W$
205	$1.2*(D + D_{platform}) + E$
206	$0.9*D + 1.6*W$
207	$0.9*D + E$

PROPRIETARY & CONFIDENTIAL

The contents of this document are the sole property of Outotec Oyj. Any rights not expressly granted herein are reserved. Reproduction, transfer or distribution of part or all of the contents in any form without the prior written permission of Outotec is prohibited.

This document is the property of LARSEN & TOUBRO and must not be passed on to any person or body not authorized by us to receive it nor be copied or otherwise made use either in full or in part by such person or body without our prior permission in writing.

MD-216-3850-EG-CV-CAL-1430	Mansourah Massarah Gold Project	Page OF
900707_GAU01_AA03_CED01_ 38503_OU100688398_R2	CALCULATION REAGENTS – LIME SLAKING EQUIPMENT MILK OF LIME DOSING TANK	Date 15.11.2023
O19045_450_C_K_24166_001_R2	AS BUILT	Rev. D01

6. SAFETY FACTOR AGAINST STABILITY

6.1 Overturning : For foundation design factor of safety against overturning is consider 2.0 for permanent load.
For foundation design factor of safety against overturning is consider 1.5 for temporary load.

6.2 Sliding : For foundation design a minimum factor of safety against sliding is consider 1.5

7. ALLOWABLE SOIL BEARING CAPACITY


The net safe bearing capacity of soil for foundations design as obtained from page 39 of Doc. No. MD-216-0000-EM-GM-RPT-0003 is 670 KN/m2 at 1.2m depth below FGL
The neareast Bore Hole of 3850-REA-001 MILK OF LIME DOSING TANK is BH-12 to BH-15.
The net safe bearing capacity of soil as per approved L&T soil test report (Table-6 of Doc. No. MD-216-3000-EG-CV-RPT-1008-A02) is 1200 KN/m2 at 1.5m depth below FGL.

However for safe design purpose we have considered the Net Safe Bearing Capacity at founding level as **670 KN/m2**.

PROPRIETARY & CONFIDENTIAL
The contents of this document are the sole property of Outotec Oyj. Any rights not expressly granted herein are reserved. Reproduction, transfer or distribution of part or all of the contents in any form without the prior written permission of Outotec is prohibited.
This document is the property of LARSEN & TOUBRO and must not be passed on to any person or body not authorized by us to receive it nor be copied or otherwise made use either in full or in part by such person or body without our prior permission in writing.

MA'ADEN معادن Saudi Arabian Mining Company شركة التعدين العربية السعودية		Outotec LARSEN & TOUBRO
MD-216-3850-EG-CV-CAL-1430	Mansourah - Massarah Gold Project	Page: of
900707_GAU01_AA03_CED01_ 38503_OU100688398_R2	DESIGN CALCULATION REAGENTS – LIME SLAKING EQUIPMENT MILK OF LIME DOSING TANK	Date: 15.11.2023
O19045_450_C_K_24166_001_R2	AS BUILT	Rev: D01

8. DESIGN OF TANK FOUNDATION (3850-REA-001 MILK OF LIME DOSING TANK)

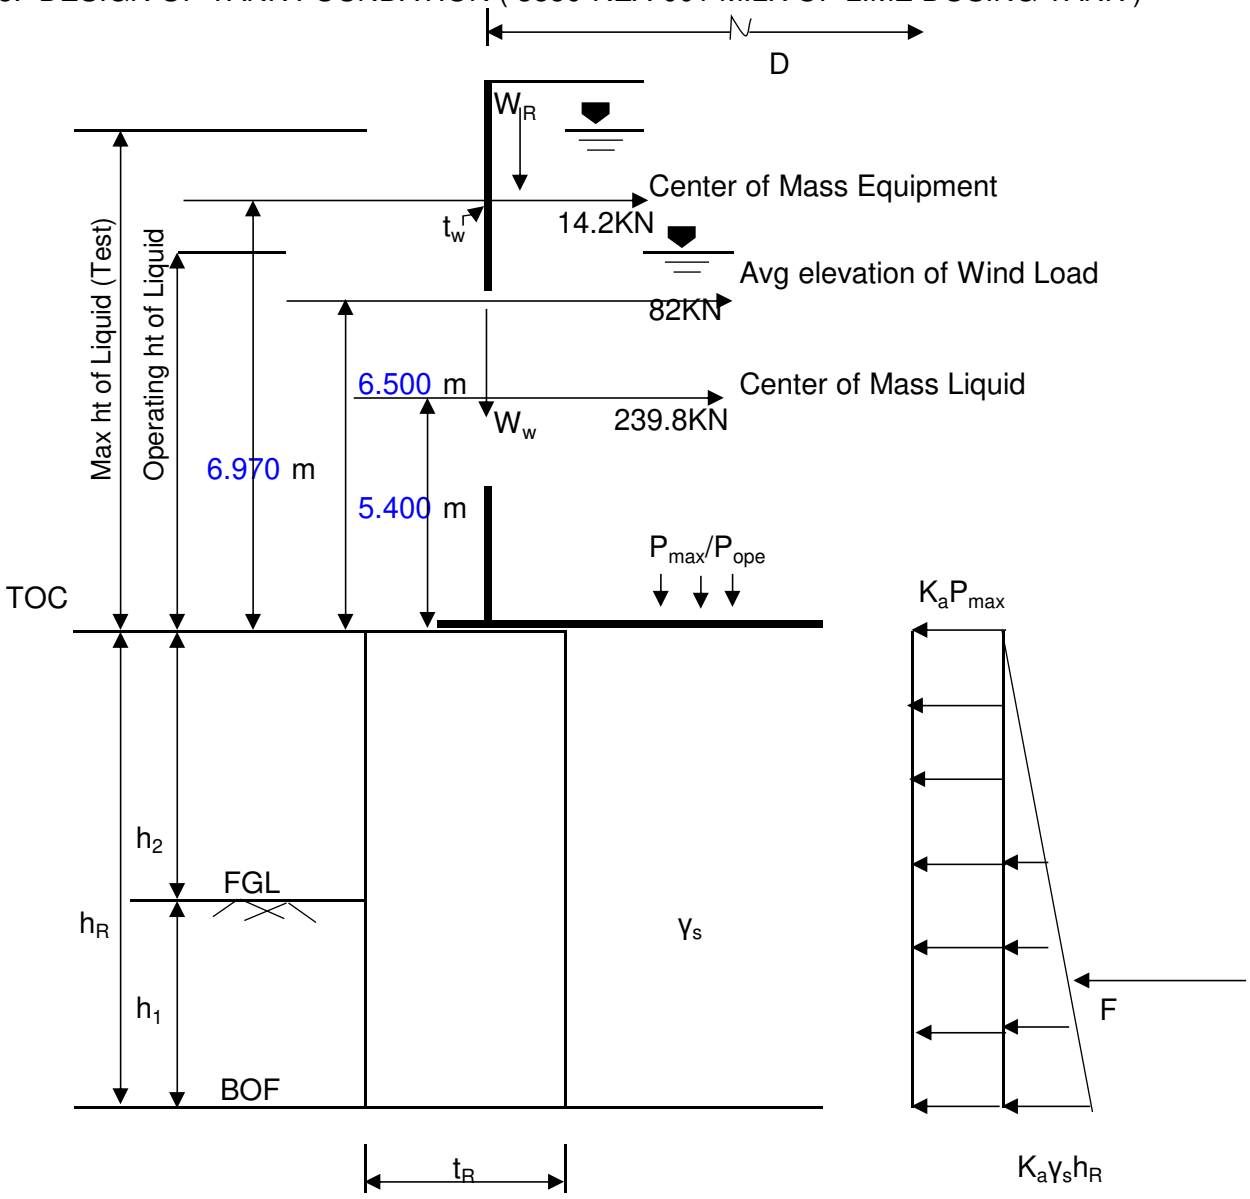

Typical Section Through Tank

Pressure on ring wall

PROPRIETARY & CONFIDENTIAL

The contents of this document are the sole property of Outotec Oyj. Any rights not expressly granted herein are reserved. Reproduction, transfer or distribution of part or all of the contents in any form without the prior written permission of Outotec is prohibited.

This document is the property of LARSEN & TOUBRO and must not be passed on to any person or body not authorized by us to receive it nor be either in copied or otherwise made use full or in part by such person or body without our prior permission in writing.

MA'ADEN معادن Saudi Arabian Mining Company شركة التعدين العربية السعودية		Outotec / LARSEN & TOUBRO
MD-216-3850-EG-CV-CAL-1430	Mansourah - Massarah Gold Project	Page: of
900707_GAU01_AA03_CED01_ 38503_OU100688398_R2	DESIGN CALCULATION REAGENTS – LIME SLAKING EQUIPMENT MILK OF LIME DOSING TANK	Date: 15.11.2023
O19045_450_C_K_24166_001_R2	AS BUILT	Rev: D01

Tank Data :

Diameter of tank ,D =	8.012	m
Self weight of tank =	324	KN
Self weight of tank per m of circumference,W_T =	12.9	KN/m
External platform weight =	27.5	KN
Platform weight per m of circumference,W_P=	1.09	KN/m
Maximum weight of Slurry (F_{max}) =	6139	KN
Pressure at base of tank , P_{max} = (F_{max}) / A =	122	KN/m^2
Operating weight of Slurry ($F_{operating}$) =	5457	KN
Pressure at base of tank , $P_{operating}$ = ($F_{operating}$) / A =	108	KN/m^2

Foundation Material :

Concrete, f_c' =	35	MPa
Reinforcement, f_y =	420	MPa
Unit weight of concrete,γ_c =	24	KN/m^3

Soil Data :

Unit weight of soil,γ_s =	19	KN/m^3	(Natural sand)
Allowable bearing pressure, q_{all}=	670	KN/m^2	
Coefficient of active earth pressure,K_a =	0.33		

Design Data of Ringwall :

Ringwall depth, $h_R = h_1 + h_2$ =	2.2	m
FGL to Bottom of foundation ,h_1 =	1.5	m
FGL to Top of concrete ,h_2 =	0.7	m
Ringwall thickness, t_R =	550	mm
Inner dia of ringwall,D_i =	7.51	m
Outer dia of ringwall,D_o =	8.61	m
$S_{xx} = \pi(D_o^4-D_i^4)/32D_o$ =	26.41	m^3

PROPRIETARY & CONFIDENTIAL

The contents of this document are the sole property of Outotec Oyj. Any rights not expressly granted herein are reserved. Reproduction, transfer or distribution of part or all of the contents in any form without the prior written permission of Outotec is prohibited.

This document is the property of LARSEN & TOUBRO and must not be passed on to any person or body not authorized by us to receive it nor be either in copied or otherwise made use full or in part by such person or body without our prior permission in writing.

MA'ADEN معادن Saudi Arabian Mining Company شركة التعدين العربية السعودية		Outotec / LARSEN & TOUBRO
MD-216-3850-EG-CV-CAL-1430	Mansourah - Massarah Gold Project	Page: of
900707_GAU01_AA03_CED01_ 38503_OU100688398_R2	DESIGN CALCULATION REAGENTS – LIME SLAKING EQUIPMENT MILK OF LIME DOSING TANK	Date: 15.11.2023
O19045_450_C_K_24166_001_R2	AS BUILT	Rev: D01

Check of soil bearing pressure (Max weight of Slurry)

Wind force = 82 KN acting at a height of 8.700 m from BOF

M_{OT} = Overturning moment = 713.4 KN-m

M_{OT} / S_{xx} = 27 KN/m^2

Load Combination : 102. $D + D_{platform} + F_{max}$

$q_{RF} = (W_T + W_P)/t_R + P_{max} + h_R\gamma_c$ = 200 KN/m^2 **< 670KN/m2, O.K.**

Load Combination : 104. $D + D_{platform} + F_{max} \pm W$

$q_{max} = q_{RF} + M_{OT}/S_{xx}$ = 227 KN/m^2 **< 670KN/m2, O.K.**

$q_{min} = q_{RF} - M_{OT}/S_{xx}$ = 173 KN/m^2

Check of soil bearing pressure (Empty Tank): For wind Load

Soil bearing pressure under ringwall :

Load Combination : 107. $0.6*(D + D_{platform}) \pm W$

$q_{RE} = (W_T + W_P)/t_R + h_R\gamma_c$ = 78.2 KN/m^2

$q_{max} = 0.6*q_{RE} + M_{OT}/S_{xx}$ = 73.9 KN/m^2 **< 670KN/m2, O.K.**

$q_{min} = 0.6*q_{RE} - M_{OT}/S_{xx}$ = 19.90 KN/m^2 **No (-)ve pressure**

Check for overturning (Empty Tank): For wind Load

M_{OT} = Overturning moment = 713.4 KN-m

M_{OR} = Restoring moment = (324+PI()*8.012*0.55*2.2*25)*8.012/2 = 4348 KN-m

FOS = M_{OR} / M_{OT} = 4348.14 / 713.4 = 6.09 **> 1.5, Hence O.K.**

Check for soil bearing pressure (Operating weight of slurry):

Seismic force at center of mass equipment = 324/(324+5457)*254 = 14.2 KN
acting at a height of 9.170 m from BOF

Seismic force at center of mass slurry = 5457/(324+5457)*254 = 239.8 KN
acting at a height of 7.600 m from BOF

M_{OT} = Overturning moment = 1953 KN-m

M_{OT} / S_{xx} = 74 KN/m^2

Load Combination : 103. $D + D_{platform} + F_{operating}$

$q_{RF} = (W_T + W_P)/t_R + P_{operating} + h_R\gamma_c$ = 186 KN/m^2 **< 670KN/m2, O.K.**

PROPRIETARY & CONFIDENTIAL

The contents of this document are the sole property of Outotec Oyj. Any rights not expressly granted herein are reserved. Reproduction, transfer or distribution of part or all of the contents in any form without the prior written permission of Outotec is prohibited.

This document is the property of LARSEN & TOUBRO and must not be passed on to any person or body not authorized by us to receive it nor be either in copied or otherwise made use full or in part by such person or body without our prior permission in writing.

MA'ADEN معادن Saudi Arabian Mining Company شركة التعدين العربية السعودية		Outotec / LARSEN & TOUBRO
MD-216-3850-EG-CV-CAL-1430	Mansourah - Massarah Gold Project	Page: of
900707_GAU01_AA03_CED01_ 38503_OU100688398_R2	DESIGN CALCULATION REAGENTS – LIME SLAKING EQUIPMENT MILK OF LIME DOSING TANK	Date: 15.11.2023
O19045_450_C_K_24166_001_R2	AS BUILT	Rev: D01

Load Combination : 107. $D + D_{platform} + F_{operating} \pm 0.7*E$

$q_{max} = q_{RF} + 0.7*M_{OT}/S_{xx}$ = 238 KN/m^2 **< 670KN/m2, O.K.**

$q_{min} = q_{RF} - 0.7*M_{OT}/S_{xx}$ = 135 KN/m^2

Load Combination : 111. $0.6*(D + D_{platform}) \pm 0.7*E$

$q_{max} = 0.6*(W_T + W_P)/t_R + 0.6*h_R\gamma_c + 0.7*M_{OT}/S_{xx}$ = 98.7 KN/m^2 **< 670KN/m2, O.K.**

$q_{max} = 0.6*(W_T + W_P)/t_R + 0.6*h_R\gamma_c - 0.7*M_{OT}/S_{xx}$ = -4.85 KN/m^2

Check for Overturning (Empty Tank): For Seismic Load

M_{OT} = Overturning moment = 1952.7 KN-m

M_{OR} = Restoring moment = (324+PI()*8.012*0.55*2.2*25)*8.012/2 = 4348 KN-m

FOS = M_{OR} / M_{OT} = 4348.14 / 1952.694 = 2.23 **> 1.5, Hence O.K.**

Ringwall Reinforcement :

Radial outward force on ringwall, $F = K_a h_R(P_{max} + \gamma_s h_R/2)$ = 104 KN/m

Hoop tension in ringwall, T = 1/2FD = 415 KN

Factored design tension, T_u= 581 KN FOS = 1.4

$A_{st,reqd} = T_u/\phi f_y$ = 1537 mm^2 ϕ = 0.9

$A_{st,min} = 0.002*\ h_R t_R$ = 2420 mm^2

$A_{st,reqd}$ (per face of ring wall)= 1210 mm^2

Required : 12 dia bar @ 206 c/c (per face)

Provide : 12 dia bar @ 150 c/c (per face)

$A_{st,\ provided}$(per face) = 1659 mm^2 **O.K.**

Vertical Reinforcement :

$A_{st,min} = 0.0012*\ t_R$ = 660 mm^2/m

$A_{st,reqd}$ (per face of ring wall)= 330 mm^2

Required : 10 dia bar @ 238 c/c (per face)

Provide : 10 dia bar @ 200 c/c (per face)

$A_{st,\ provided}$(per face) = 393 mm^2 **O.K.**

PROPRIETARY & CONFIDENTIAL

The contents of this document are the sole property of Outotec Oyj. Any rights not expressly granted herein are reserved. Reproduction, transfer or distribution of part or all of the contents in any form without the prior written permission of Outotec is prohibited.

This document is the property of LARSEN & TOUBRO and must not be passed on to any person or body not authorized by us to receive it nor be either in copied or otherwise made use full or in part by such person or body without our prior permission in writing.

MA'ADEN Saudi Arabian Mining Company معادن شركة التعدين العربية السعودية		Outotec LARSEN & TOUBRO
MD-216-3850-EG-CV-CAL-1430	Mansourah Massarah Gold Project	Page OF
900707_GAU01_AA03_CED01_ 38503_OU100688398_R2	CALCULATION REAGENTS – LIME SLAKING EQUIPMENT MILK OF LIME DOSING TANK	Date 15.11.2023
O19045_450_C_K_24166_001_R2	AS BUILT	Rev. D01

ATTACHMENT - 1 : Mechanical Input Drawing.


PROPRIETARY & CONFIDENTIAL

The contents of this document are the sole property of Outotec Oyj. Any rights not expressly granted herein are reserved. Reproduction, transfer or distribution of part or all of the contents in any form without the prior written permission of Outotec is prohibited.


This document is the property of LARSEN & TOUBRO and must not be passed on to any person or body not authorized by us to receive it nor be copied or otherwise made use either in full or in part by such person or body without our prior permission in writing.


DRAWING NUMBER	REV
MD-216-3850-EG-ME-PLN-1001	D01

LOADING NOTES:	
1.	THE LOWEST NATURAL FREQUENCY OF COMBINED MACHINE, FLUID LOAD, AND SUPPORT SYSTEM IN ANY DIRECTION MUST EXCEED 1.5 TIMES THE ROTOR ROTATIONAL FREQUENCY (REFER NORMAL OPERATING SPEED*)
2.	ALL LOADS ASSUME UNIFORM SUPPORT OF TANK BASE. (TANK LOCATED ON THE GROUND OR CONCRETE SLAB)
3.	REPORTED SEISMIC LOADS ARE PRIMARY LOADS WITH A COMBINATION FACTOR OF 1.0 SUITABLE FOR STRENGTH DESIGN DERIVED IN ACCORDANCE WITH THE SITE SPECIFICATIONS AND THE REQUIREMENTS OF SBC 301 - 2007. HOWEVER IF THE LOADS ARE TO BE USED FOR ALLOWABLE STRESS DESIGN FOR FOUNDATION DESIGN THEN THE COMBINATION FACTOR WOULD BE 0.7 AND TO BE APPLIED BY CIVIL DESIGNERACCORDING SBC 301 - 2007.
4.	REPORTED WIND LOADS ARE PRIMARY UNFACTORED LOADS SUITABLE FOR LOAD COMBINATIONS TO SBC 301 - 2007. CIVIL DESIGNER TO APPLY COMBINATION FACTOR OF 1.6 FOR STRENGTH DESIGN
FOUNDATION AND SUPPORT TOLERANCES	
1.	THE FIRST 300mm WIDTH OF AN ANNULAR RING MEASURED FROM THE OUTSIDE OF THE TANK RADIALLY TOWARDS THE CENTRE SHALL BE WITHIN +/-3mm OF THE DESIGN LEVEL
2.	THE REMAINDER OF THE FOUNDATION SHALL BE WITHIN +/-6mm OF THE DESIGN LEVEL
CONCRETE NOTES: (WHERE SHELLS ARE INSTALLED ON CONCRETE AND HOLD DOWN BOLTS ARE USED)	
1.	CONCRETE FOUNDATION OUTLINE SHOWN GIVES NOMINAL EDGE DISTANCE FOR HOLD-DOWN BOLT TO EDGE OF FOUNDATION AT 110mm
2.	FINAL OVERALL CONCRETE FOUNDATION DIMENSION AND REQUIRED HOLD-DOWNBOLT EDGE DISTANCE TO BE DETERMINED BY CLIENT

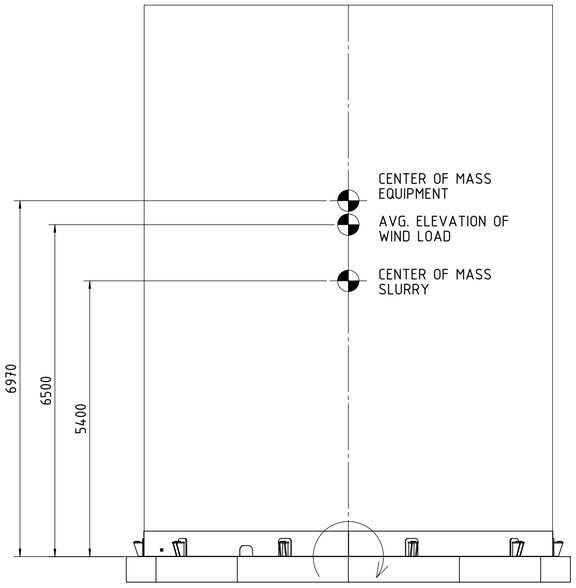

SCALE 1 : 60

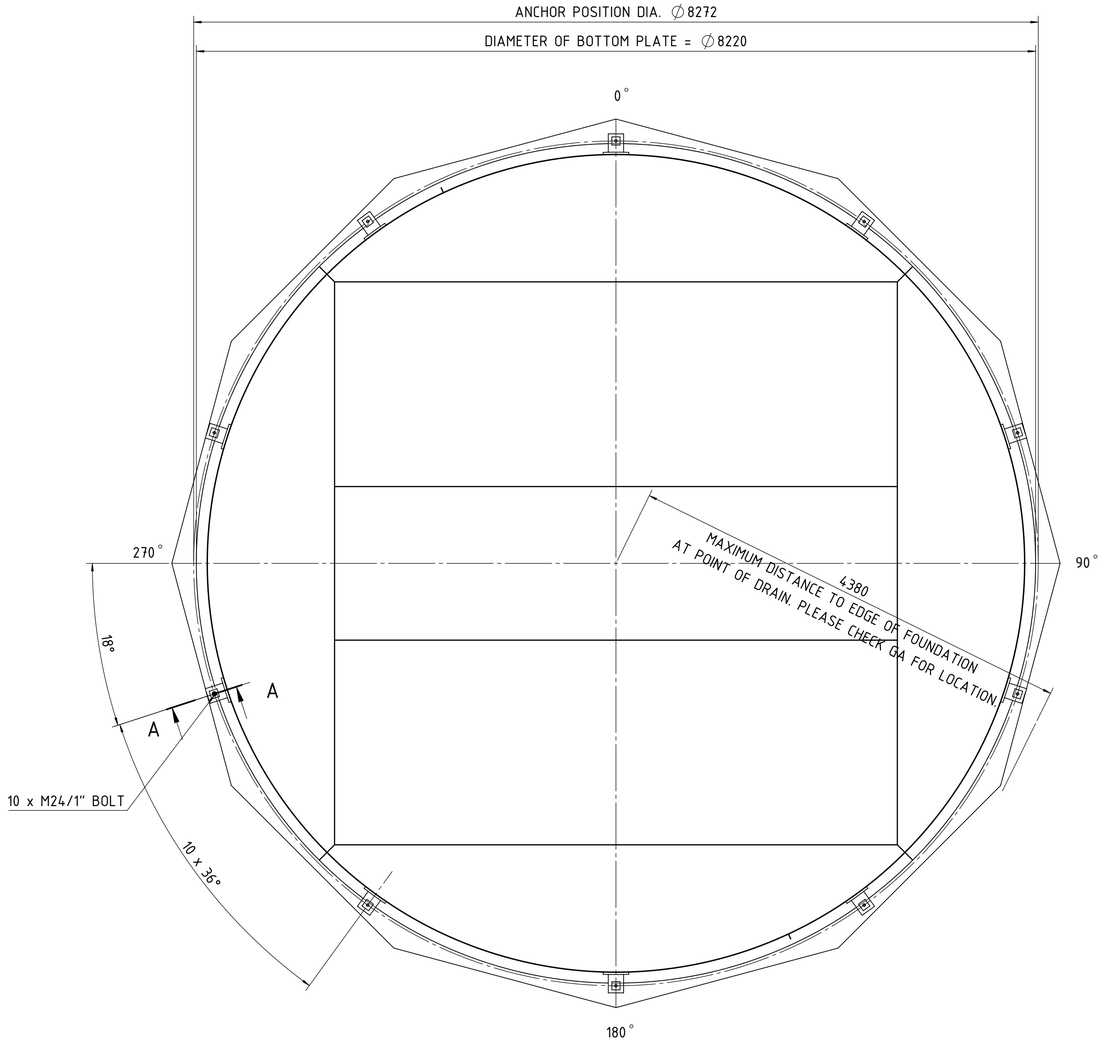

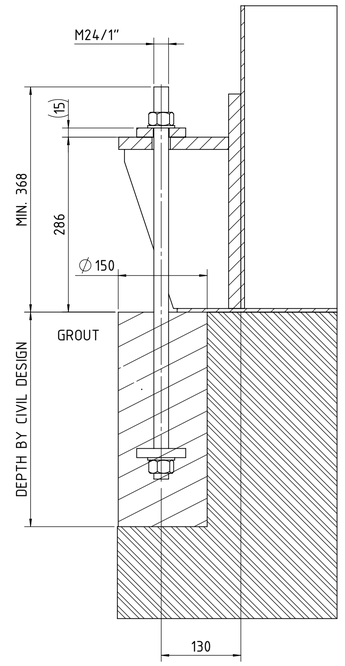

SECTION A-A
SCALE 1 : 5

MILK OF LIME DOSING TANK	
DEAD WEIGHT OF EQUIPMENT	32400 kg
OPERATIONAL WEIGHT OF SLURRY	545700 kg
MAXIMUM WEIGHT OF SLURRY	613900 kg
EXTERNAL PLATFORM LOAD	2750 kg
NORMAL OPERATING SPEED	34 rpm
WIND LOAD	82 kN
SEISMIC LOAD	254 kN
SEISMIC TORQUE AT FOUNDATION LEVEL	1389 kNm

SEISMIC LOAD IS CALCULATED WITH FOLLOWING VALUES
-S1=0.02g
-Ss=0,10g
-max. ground elevation 3m
CIVIL ENGINEERING TO CHECK SEISMIC LOAD AT ACTUAL ELEVATION

WIND LOAD IS CALCULATED WITH WIND SPEED OF 43 m/s

DOCUMENT NUMBER	REFERENCE DOCUMENTS	REV	DATE	REVISION DESCRIPTION	DRN	CHK	ENG	APP	EMP
MD-216-3850-EG-ME-GAD-1001	GENERAL ARRANGEMENT DRAWING								
MD-216-3850-EG-ME-DAT-1002	EQUIPMENT DATASHEET	D01	15.11.2023	AS BUILT	VP	TM	JR	GR	
MD-216-3850-EG-PR-PID-1002	P&I DIAGRAM	C01	03.03.2020	APPROVED FOR CONSTRUCTION	VP	TM	JR	GR	
MD-216-3850-EG-PR-PFD-1001	PROCESS FLOW DIAGRAM	A01	15.01.2020	ISSUED FOR APPROVAL	JJ	TM	JR	GR	

RESERVED FOR VENDOR LOGO AND DRAWING NUMBER

LARSEN & TOUBRO

This drawing is the property of *LARSEN & TOUBRO* and must not be passed on to any person or body not authorized by us to receive it nor be copied or otherwise made use either in full or in part by such person or body without our prior permission in writing.

Outotec

The content of these documents are the sole property of Outotec Oyj. Any rights not expressly granted herein are reserved. Reproduction, transfer or distribution of part or all of the contents in any form without prior written permission of Outotec is prohibited.

MA'ADEN معادن
Saudi Arabian Mining Company شركة المعادن العربية السعودية


This document and the information contained herein is Ma'aden proprietary know-how. This document or any part thereof should not be reproduced, stored in a retrieval system or transmitted by any means, electronic or otherwise, or divulged without prior written permission of Ma'aden.

DRAWN	vilpoy	27.02.2020	MANSOURAH-MASSARAH GOLD PROJECT
CHECKED	tuoman	03.03.2020	FOUNDATION AND LOAD PLAN
ENGINEER	juhris	03.03.2020	LIME MILK PREPARATION
APPROVED	GeoRie	03.03.2020	3850-REA-001 MILK OF LIME DOSING TANK
EMPLOYER			
SCALE	1:30	A1	


LARSEN & TOUBRO DRAWING NUMBER: 019045-450-M-D-03215-001 — REVISION: 3
OUTOTEC DRAWING NUMBER: 900707 GAU01 AA03 MLD15 38501 — DOCUMENT ID: OU601267234 — REVISION: 3
DRAWING NUMBER: MD-216-3850-EG-ME-PLN-1001 — REV: D01

DRAWING NUMBER MD-216-3850-EG-CV-GAD-1001 REV A01


LEVEL +912.350
1:50

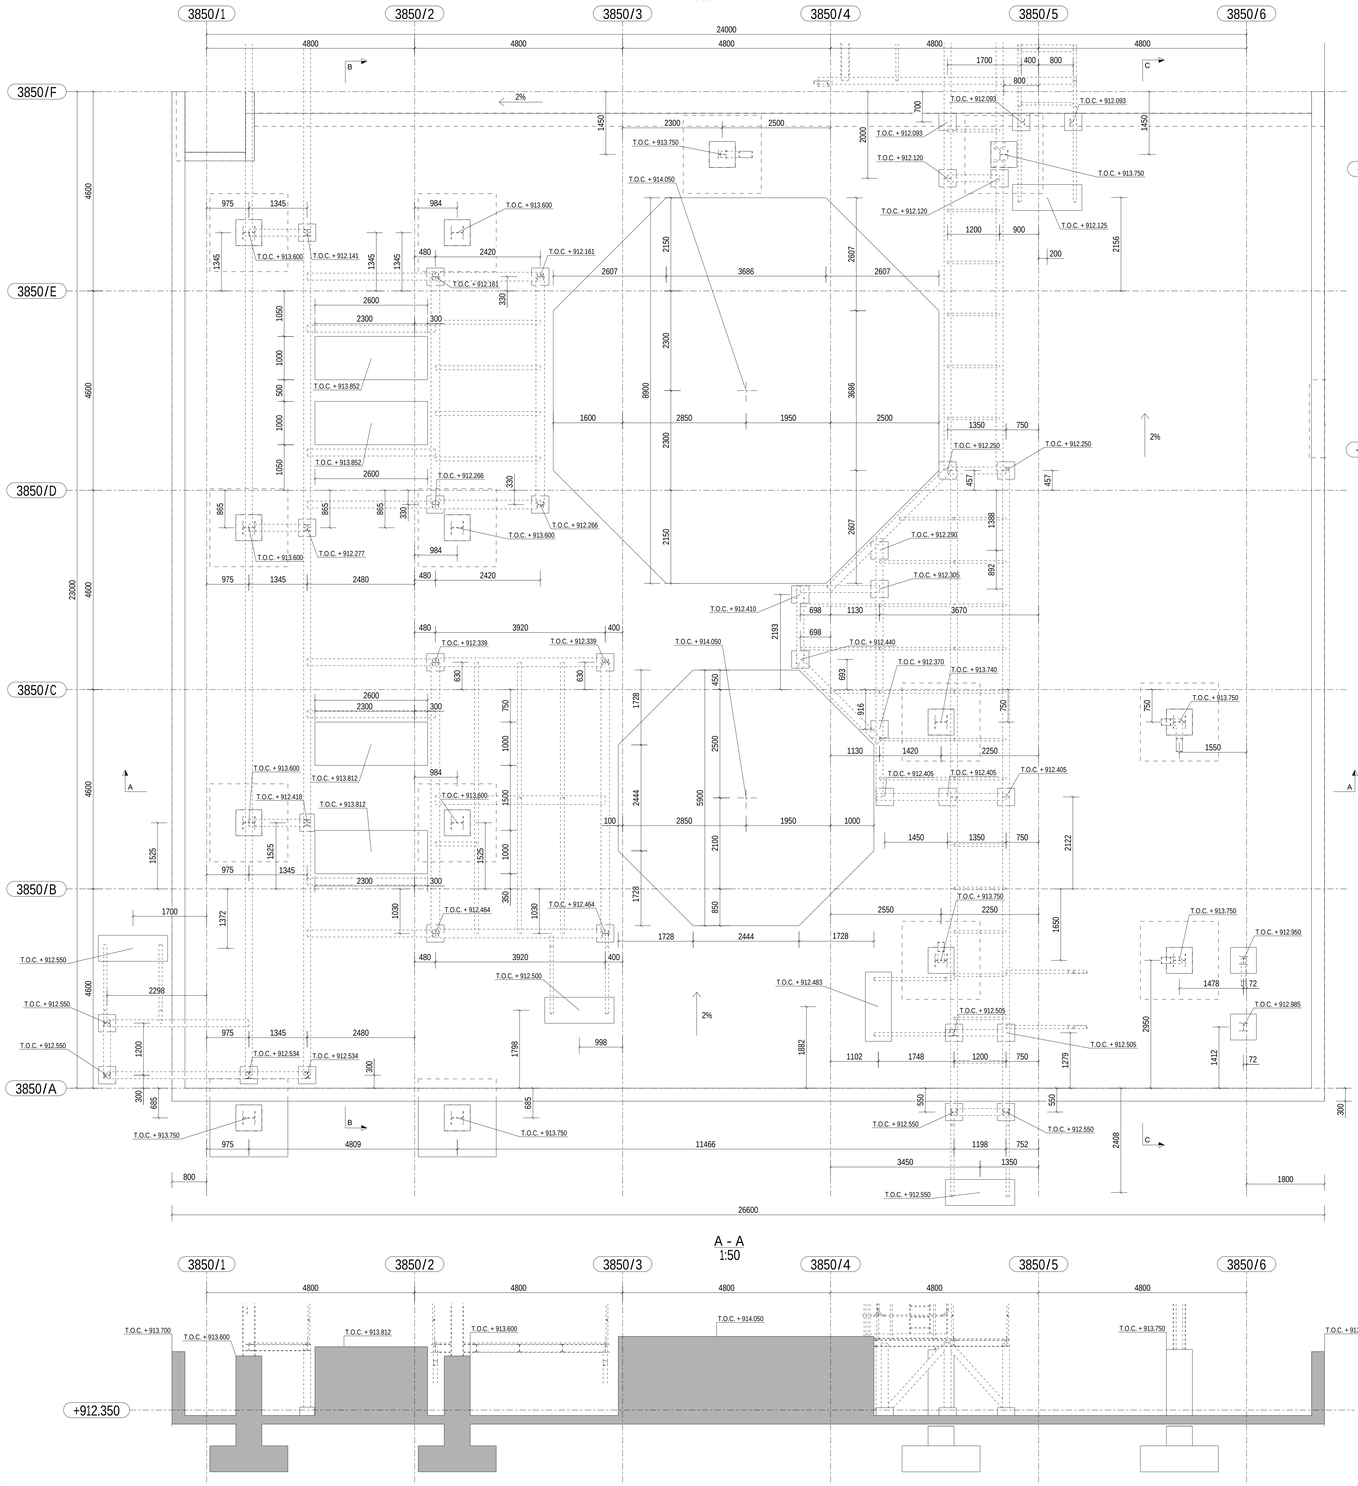


B - B
1:50

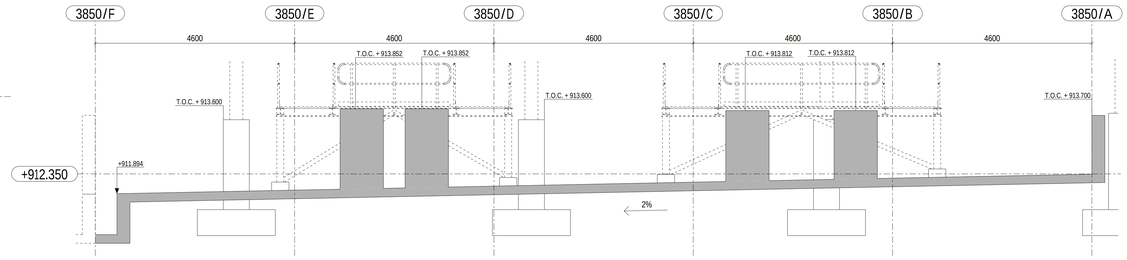

C - C
1:50

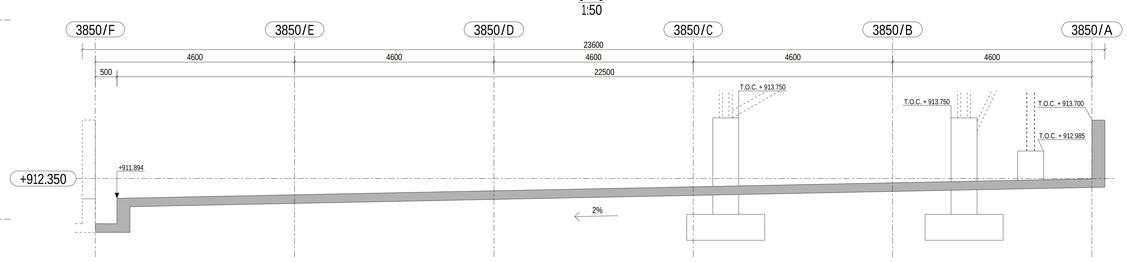

LEVEL +912.350
1:50

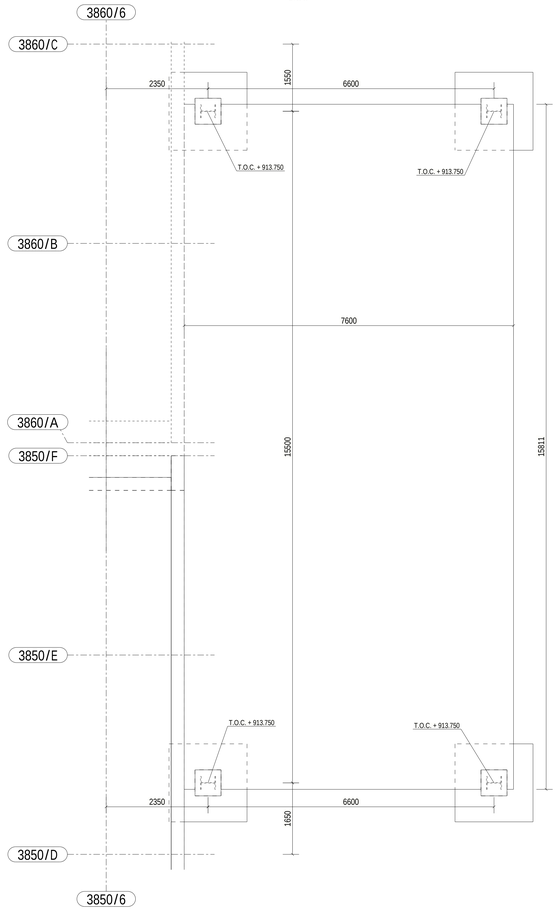

THIS DESIGN IS NOT ISSUED FOR CONSTRUCTION

FINISHED TOP GROUND LEVEL (F.G.L) FOR PROCESS AREA 3860 = RL(+)912.350 m

Document Number
MD-216-3850-EG-CV-GAD-1001

Revision A01

Approved


Mr Doron Golan - Bechtel Global
Mar 4, 2020, 4:57 PM GMT+2:00

Permission to proceed does not constitute acceptance or approval of design detail, calculations, analysis, test methods, or materials developed or selected by the Supplier, and does not relieve the Supplier from full compliance with contractual obligations

CONCRETE ELEMENT FLOOR (PRE-CAST SLAB)
CONCRETE FLOOR
CONCRETE FLOOR WITH ACID RESISTANT COATING
CONCRETE WALL

1. ALL DIMENSIONS ARE IN MILLIMETER, ELEVATIONS ARE IN METER UNLESS OTHERWISE STATED
2. CO-ORDINATES ARE SHOWN IN GENERAL ARRENGEMENT DRAWINGS
3. GRATING TYPE (FRP OR NORMAL) IS SPECIFIED IN GENERAL ARRENGEMENT DRAWINGS
4. F.F.L, F.G.L, T.O.C = FINISHED FLOOR LEVEL, FINISHED GROUND LEVEL, TOP OF CONCRETE, T.O.S, B.O.S, B.O.B, = TOP OF STEEL, BOTTOM OF STEEL, BOTTOM OF BASE PLATE
5. BUILDING DIMENSIONS AND HEIGHTS ARE TENTATIVE, SHALL BE FINALIZED DURING DETAIL ENGINEERING SUBJECT TO MINIMUM AS SHOWN.
6. ALL MAINTENANCE FACILITIES, HANDLING PROVISIONS, ACCESS WAYS, PLATFORMS FOR MAINTENANCE SHALL BE PROVIDED DURING DETAIL ENGINEERING WHICH ARE NOT SHOWN ENTIRELY. THIS DRAWING IS TO BE CONSIDERED AS CONCEPTUAL ARRANGEMENT OF THE FACILITIES.

KEYPLAN

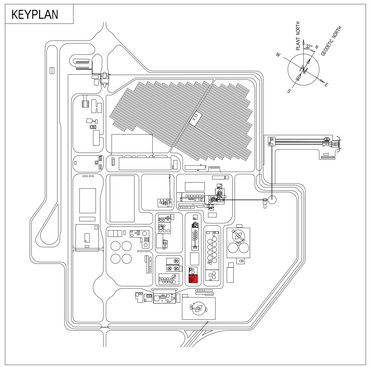

A - A
1:50

DOCUMENT NUMBER	REFERENCE DOCUMENTS	DOCUMENT NUMBER	REFERENCE DOCUMENTS
MD-216-3850-EG-ST-GAD-1002	PLAN VIEW 3850/3860/3-6/A-F,A-C, 3D AND SECTIONS		
MD-216-1000-EG-ST-CRT-0001	CIVIL/STRUCTURAL AND ARCHITECTURAL DESIGN BASIS	MD-216-3850-EG-ST-GAD-1001	PLAN VIEW 3850/1-3/A-F, 3D VIEW AND SECTIONS
MD-216-3850-EG-ME-GAD-1008	SECTION B-B	MD-216-3850-EG-ME-GAD-1009	SECTION C-C
MD-216-3850-EG-ME-GAD-1006	PLAN VIEW	MD-216-3850-EG-ME-GAD-1007	SECTION A-A
MD-216-3850-EG-ME-GAD-1004	PLAN AT EL. +912.350	MD-216-3850-EG-ME-GAD-1005	PLAN AT EL. +919.990

REV	DATE	REVISION DESCRIPTION	DRN	CHK	ENG	APP	EMP
A01	07.02.2020	ISSUED FOR APPROVAL	KirJok	MikLai	LuiPiz	SuoCha	

RESERVED FOR VENDOR LOGO AND DRAWING NUMBER

LARSEN & TOUBRO

This drawing is the property of LARSEN & TOUBRO and must not be passed on to any person or body not authorized by us to receive it nor be copied or otherwise made use either in full or in part by such person or body without our prior permission in writing.

Outotec

The content of these documents are the sole property of Outotec Oy. Any rights not expressly granted herein are reserved. Reproduction, transfer or distribution of part or all of the contents in any form without prior written permission of Outotec is prohibited.

MA'ADEN معادن
Saudi Arabian Mining Company شركة معادن السعودية

This document and the information contained herein is Ma'aden proprietary know-how. This document or any part thereof should not be reproduced, stored in a retrieval system or transmitted by any means, electronic or otherwise, or divulged without prior written permission of Ma'aden.

LARSEN & TOUBRO DRAWING NUMBER: 900707_GAU01_AA03_CTA04_38501 — REVISION: 0
OUTOTEC DRAWING NUMBER: OU100668289 — REVISION: 0


DRAWN	KirJok	07.02.2020
CHECKED	MikLai	07.02.2020
ENGINEER	LuiPiz	07.02.2020
APPROVED	SuoCha	07.02.2020
EMPLOYER		
SCALE	1:50	A0


MANSOURAH - MASSARAH GOLD PROJECT
CIVIL WORKS GUIDE DRAWING
LIME SLAKING
PLAN AT EL. +912.350 AND SECTIONS

DRAWING NUMBER: MD-216-3850-EG-CV-GAD-1001 — REV: A01

Tekla Structures

DRAWING NUMBER: MD-216-3850-EG-ME-GAD-1004 | REV: A02

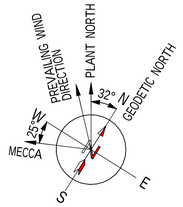

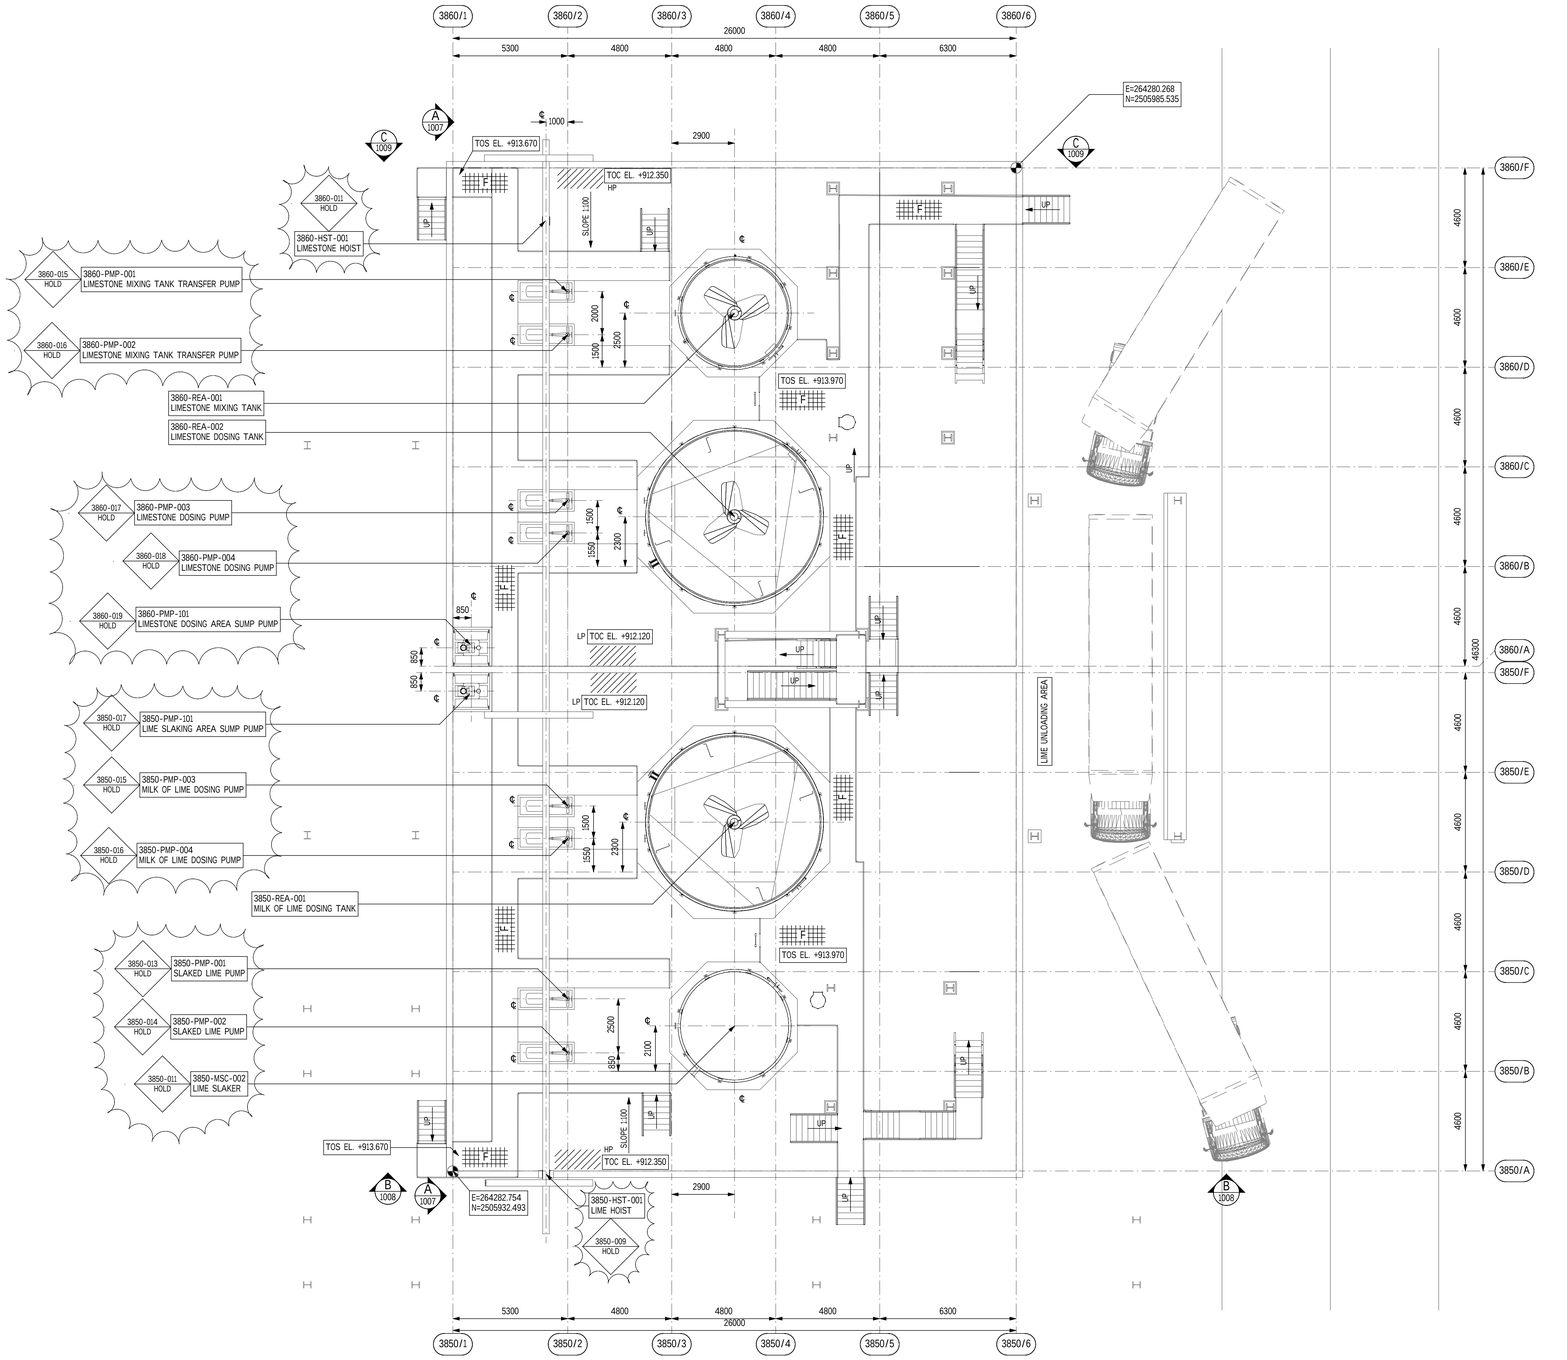


PLAN AT EL.(+)912.350

- CONCRETE ELEMENT FLOOR (PRE-CAST SLAB)
- CONCRETE FLOOR
- CONCRETE FLOOR WITH ACID RESISTANT COATING
- CHECKERED PLATE
- GRATING
- GRATING - FRP
- ACID RESISTANT BRICKLINING
- BRICK WALL
- CONCRETE WALL

1. ALL DIMENSIONS ARE IN MILLIMETER, CO-ORDINATES AND ELEVATION ARE IN METERS UNLESS OTHERWISE STATED.
2. FINISHED GROUND LEVEL (F.G.L) FOR PROCESS AREA 3850 & 3860 = RL(+)912.350 m
3. F.F.L, F.G.L, T.O.C = FINISHED FLOOR LEVEL, FINISHED GROUND LEVEL, TOP OF CONCRETE. T.O.S, B.O.S, B.O.B, = TOP OF STEEL, BOTTOM OF STEEL, BOTTOM OF BASE PLATE. T.O.G. = TOP OF GRATING. HP = HIGHT POINT, LP = LOW POINT, T.O.R. = TOP OF RAIL.
4. BUILDING DIMENSIONS AND HEIGHTS ARE TENTATIVE, SHALL BE FINALIZED DURING DETAIL ENGINEERING SUBJECT TO MINIMUM AS SHOWN.
5. ALL MAINTENANCE FACILITIES, HANDLING PROVISIONS, ACCESS WAYS, PLATFORMS FOR MAINTENANCE SHALL BE PROVIDED DURING DETAIL ENGINEERING WHICH ARE NOT SHOWN ENTIRELY. THIS DRAWING IS TO BE CONSIDERED AS CONCEPTUAL ARRANGEMENT OF THE FACILITIES.

KEYPLAN

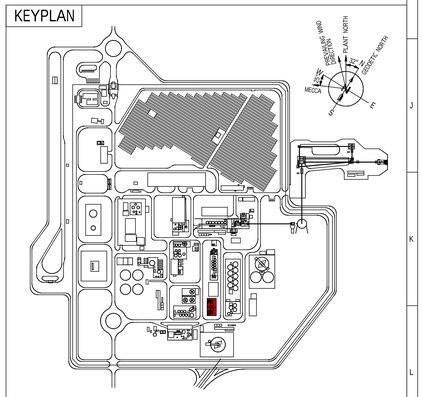

0 1 10m

DOCUMENT NUMBER	REFERENCE DOCUMENTS
MD-216-3000-EG-GM-LST-1010	HOLD LIST
MD-216-3850-EG-ME-GAD-1009	SECTION C-C
MD-216-3850-EG-ME-GAD-1008	SECTION B-B
MD-216-3850-EG-ME-GAD-1007	SECTION A-A
MD-216-3850-EG-ME-GAD-1006	PLAN VIEW
MD-216-3850-EG-ME-GAD-1005	PLAN AT EL. +919.990

REV	DATE	REVISION DESCRIPTION	DRN	CHK	ENG	APP	EMP
A02	04-02-2020	ISSUED FOR DESIGN	SS	TV	SC	RL	
A01	15-10-2019	ISSUED FOR APPROVAL	AM	TV	SC	RL	

REVISION DESCRIPTION | DRN | CHK | ENG | APP | EMP | REV | DATE

RESERVED FOR VENDOR LOGO AND DRAWING NUMBER

LARSEN & TOUBRO
This drawing is the property of LARSEN & TOUBRO and must not be passed on to any person or body not authorized by us to receive it or be copied or otherwise made use either in full or in part by such person or body without our prior permission in writing.

Outotec
The content of these documents are the sole property of Outotec Oyj. Any rights not expressly granted herein are reserved. Reproduction, transfer or distribution of part or all of the contents in any form without prior written permission of Outotec is prohibited.

MA'ADEN معادن
Saudi Arabian Mining Company
This document and the information contained herein is Ma'aden proprietary know-how. This document or any part thereof should not be reproduced, stored in a retrieval system or transmitted by any means, electronic or otherwise, or divulged without prior written permission of Ma'aden.

LARSEN & TOUBRO DRAWING NUMBER	O19045_450_M_G_03255_001		REVISION 1
OUTOTEC DRAWING NUMBER	900707 _GAU01 _AA03_ MTL01 _38501	DOCUMENT ID OU100664249	REVISION 1

DRAWN	AM	15-10-2019	MANSOURAH-MASSARAH GOLD PROJECT
CHECKED	TV	15-10-2019	GENERAL ARRANGEMENT DRAWING
ENGINEER	SC	15-10-2019	REAGENTS - LIME SLAKING AND LIMESTONE
APPROVED	RL	15-10-2019	PLAN AT EL. +912.350
EMPLOYER			DRAWING NUMBER: MD-216-3850-EG-ME-GAD-1004 REV A02
SCALE	1:100	A0	